LORITZ
LYCÉE D'ENSEIGNEMENT GÉNÉRAL ET TECHNOLOGIQUE
CFA - GRETA

L'INVENTAIRE

Département des Vosges (88)

Ville de Gelvécourt-et-Adompt

La Région Grand Est

Plan d'intérieur

1 Rue du Village, à Gelvécourt-et-Adompt 88270

PLAN DU SOUS SOL

Echelle : 1/50
Date : 05/04/2023
Dessinateur : SICHLER Calvin

Réf.DAO	Nat	Indice
2023 88 10350 NUDA		

Ind.	Date	Statut	NATURE	Dessiné par	Vérifié par	Approuvé par
	05/04/2023		Plan du sous sol	LORL1		

MURS
SENS DE CIRCULATION
S=26m² SURFACES
3.01 COTATIONS (m)
h:4.40m HAUTEURS

N

Rle des Marronniers

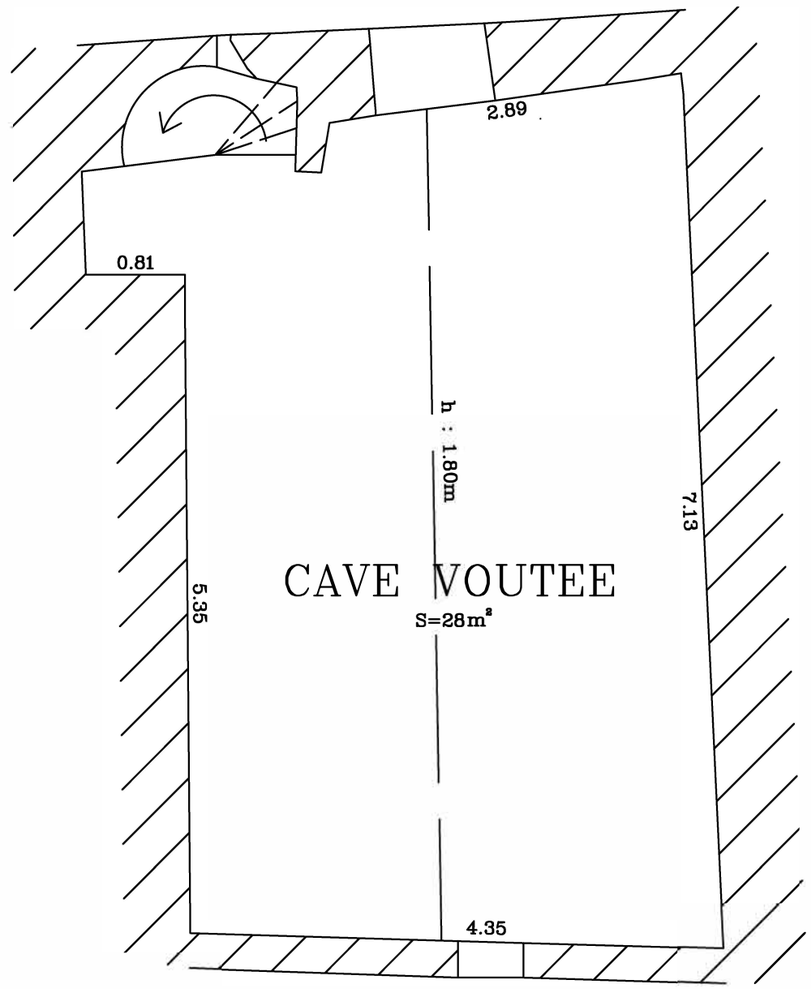

Rue de l'Église

0 1 5m

MURS

PORTES

SENS DE CIRCULATION

S=26m² SURFACES

3.01 COTATIONS (m)

h:4.40m HAUTEURS

LORITZ
LYCÉE D'ENSEIGNEMENT GÉNÉRAL ET TECHNOLOGIQUE
CFA - GRETA

L'INVENTAIRE

Département des Vosges (88)

Ville de Gelvécourt-et-Adompt

La Région Grand Est

Plan d'intérieur

1 Rue du Village, à Gelvécourt-et-Adompt 88270

PLAN DES COMBLES

Echelle : 1/50
Date : 05/04/2023
Dessinateur : LIEGEON Théo

Réf.DAO	Nat	Indice
2023 88 10353 NUDA		

Ind.	Date	Statut	NATURE	Dessiné par	Vérifié par	Approuvé par
	05/04/2023		Plan des combles	LORL1		

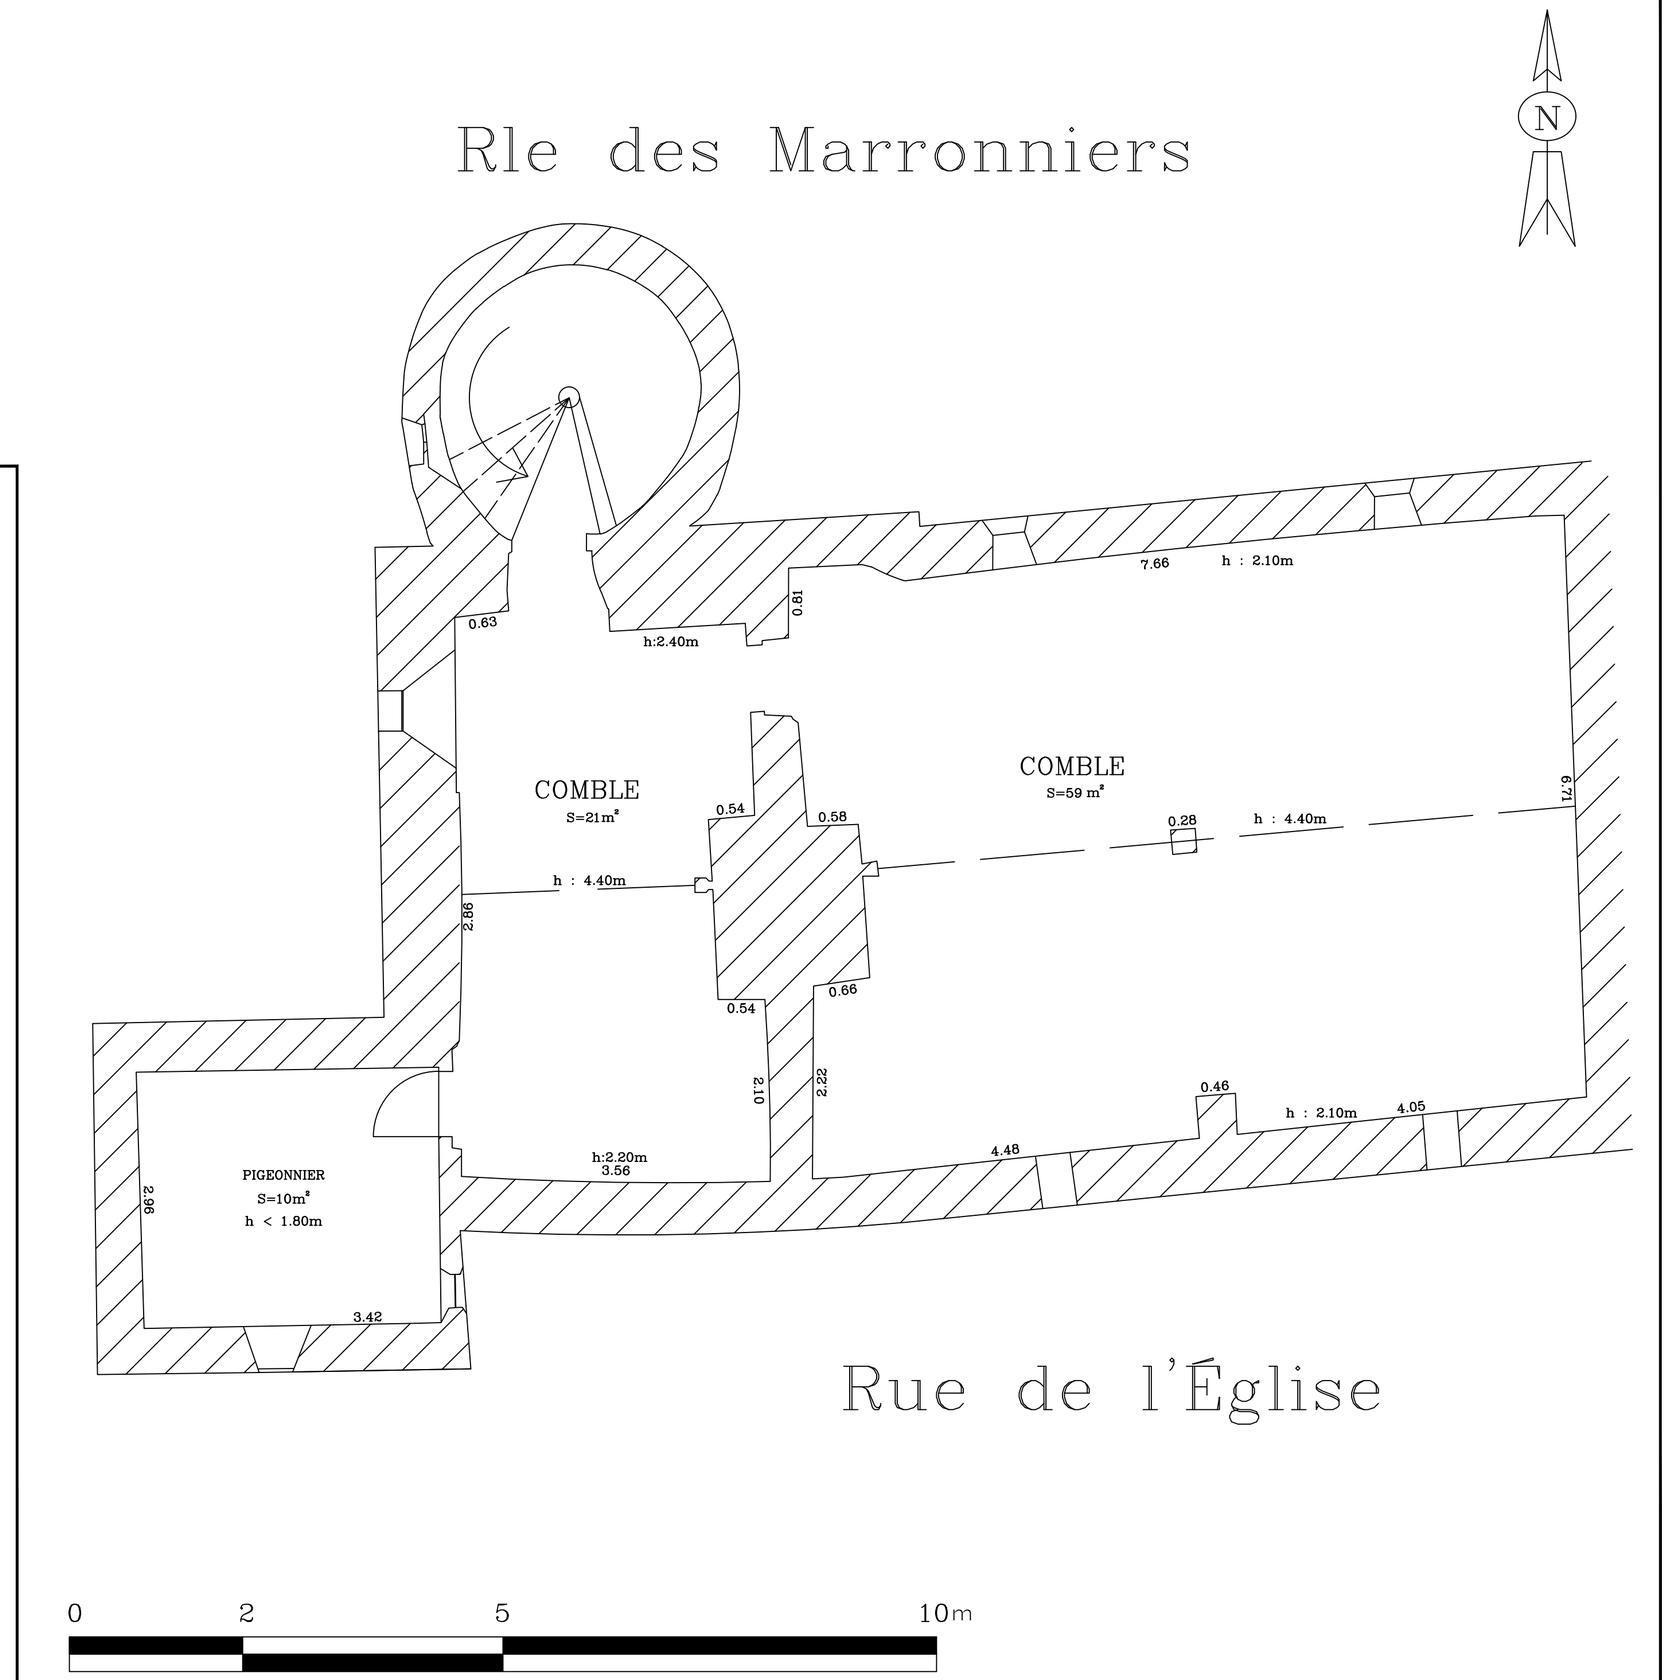

MURS

PORTES

SENS DE CIRCULATION

S=26m² SURFACES

3.01 COTATIONS (m)

(2.00) ELEVATIONS (m)

LORITZ
LYCÉE D'ENSEIGNEMENT GÉNÉRAL ET TECHNOLOGIQUE
CFA - GRETA

L'INVENTAIRE

Département des Vosges (88)

Ville de Gelvécourt-et-Adompt

La Région Grand Est

Plan d'intérieur

1 Rue du Village, à Gelvécourt-et-Adompt 88270

PLAN DU PREMIER ETAGE

Echelle : 1/50
Date : 05/04/2023
Dessinateur : LIEGEON Théo

Réf.DAO	Nat	Indice
2023 88 10352 NUDA		

Ind.	Date	Statut	NATURE	Dessiné par	Vérifié par	Approuvé par
	05/04/2023		Plan du premier étage	LORL1		

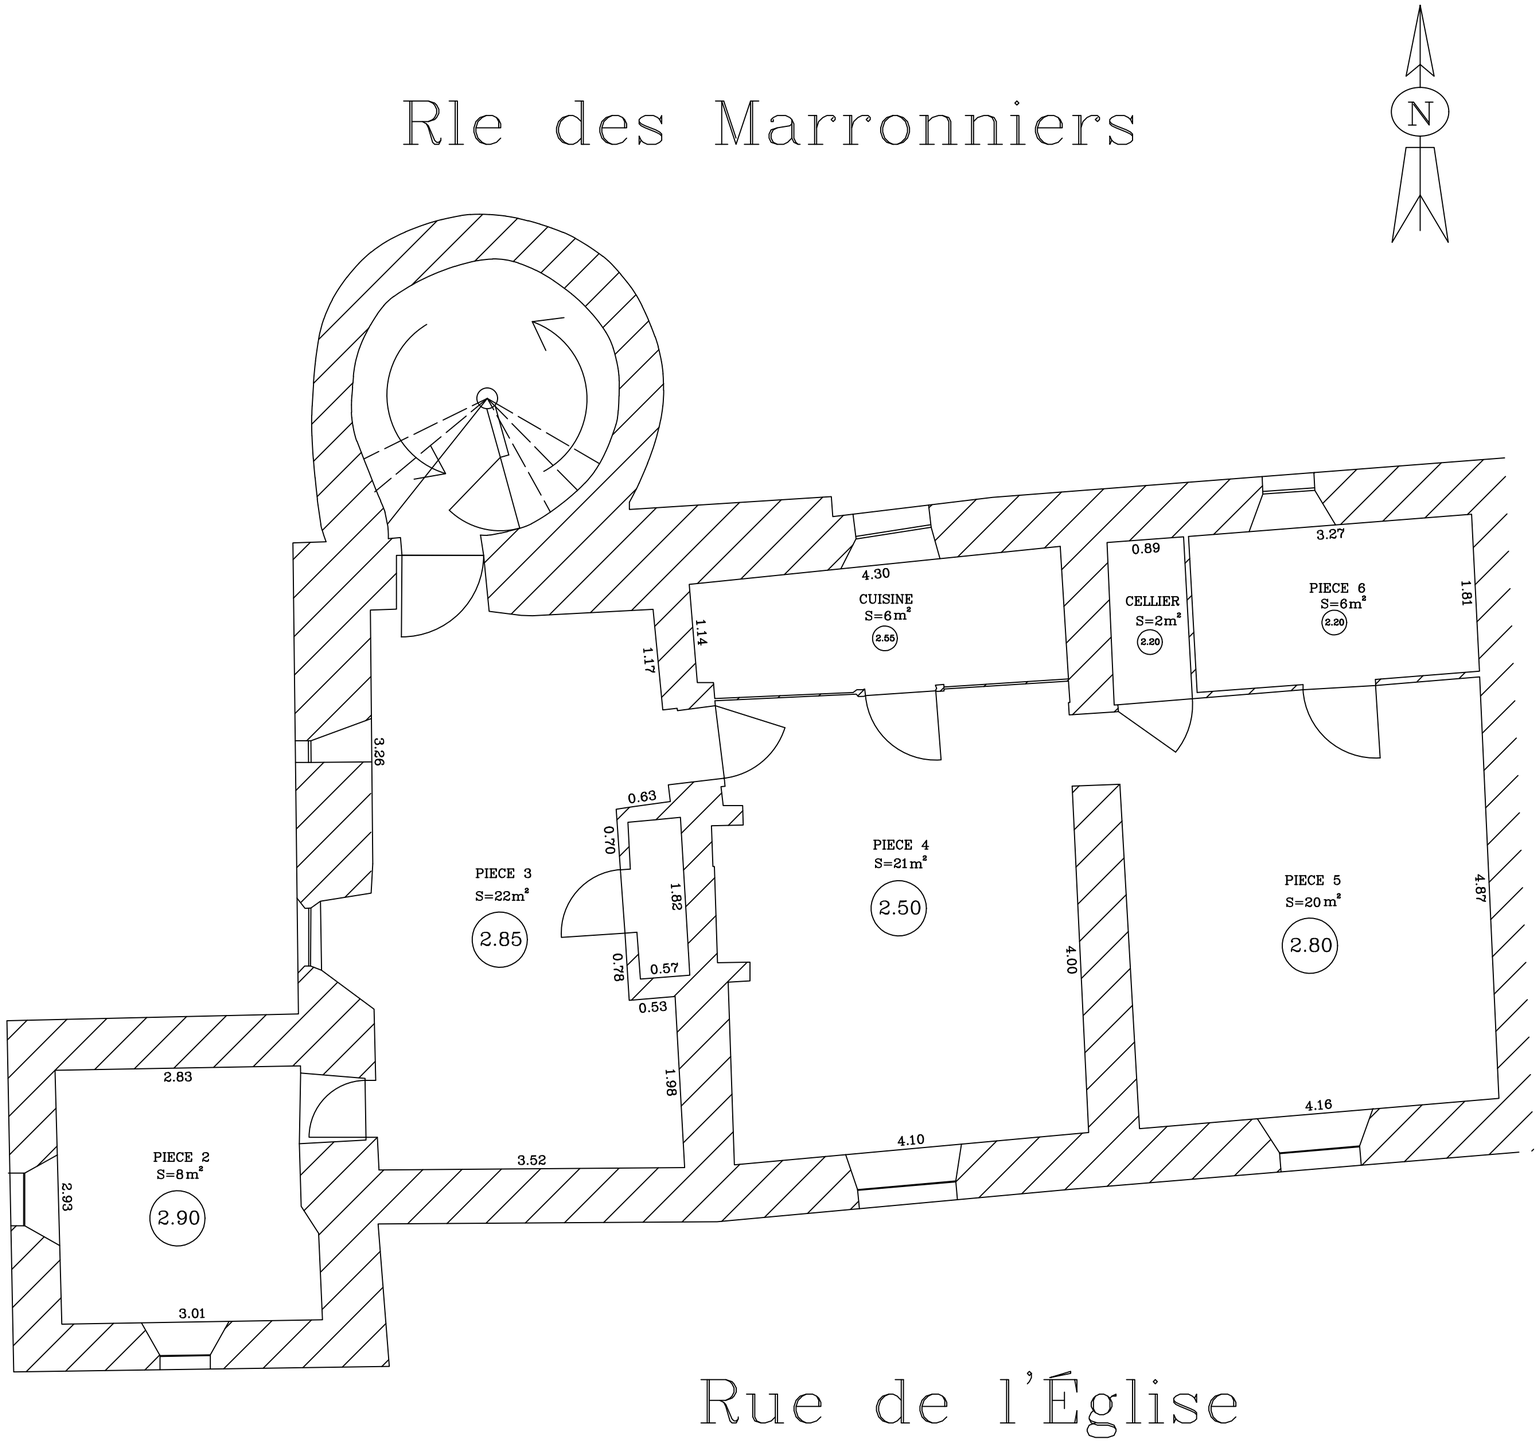

0 2 5 10 m

MURS

PORTES

SENS DE CIRCULATION

S=26m² SURFACES

3.01 COTATIONS (m)

(2.00) ELEVATIONS (m)

LORITZ
LYCÉE D'ENSEIGNEMENT GÉNÉRAL ET TECHNOLOGIQUE
CFA - GRETA

L'INVENTAIRE

Département des Vosges (88)

Ville de Gelvécourt-et-Adompt

La Région Grand Est

Plan d'intérieur

1 Rue du Village, à Gelvécourt-et-Adompt 88270

PLAN DU REZ-DE-CHAUSSEE

Echelle : 1/50
Date : 05/04/2023
Dessinateur : LIEGEON Théo

Réf.DAO	Nat	Indice
2023 88 10351 NUDA		

Ind.	Date	Statut	NATURE	Dessiné par	Vérifié par	Approuvé par
	05/04/2023		Plan du rez-de-chaussée	LORL1		

Rle des Marronniers

N

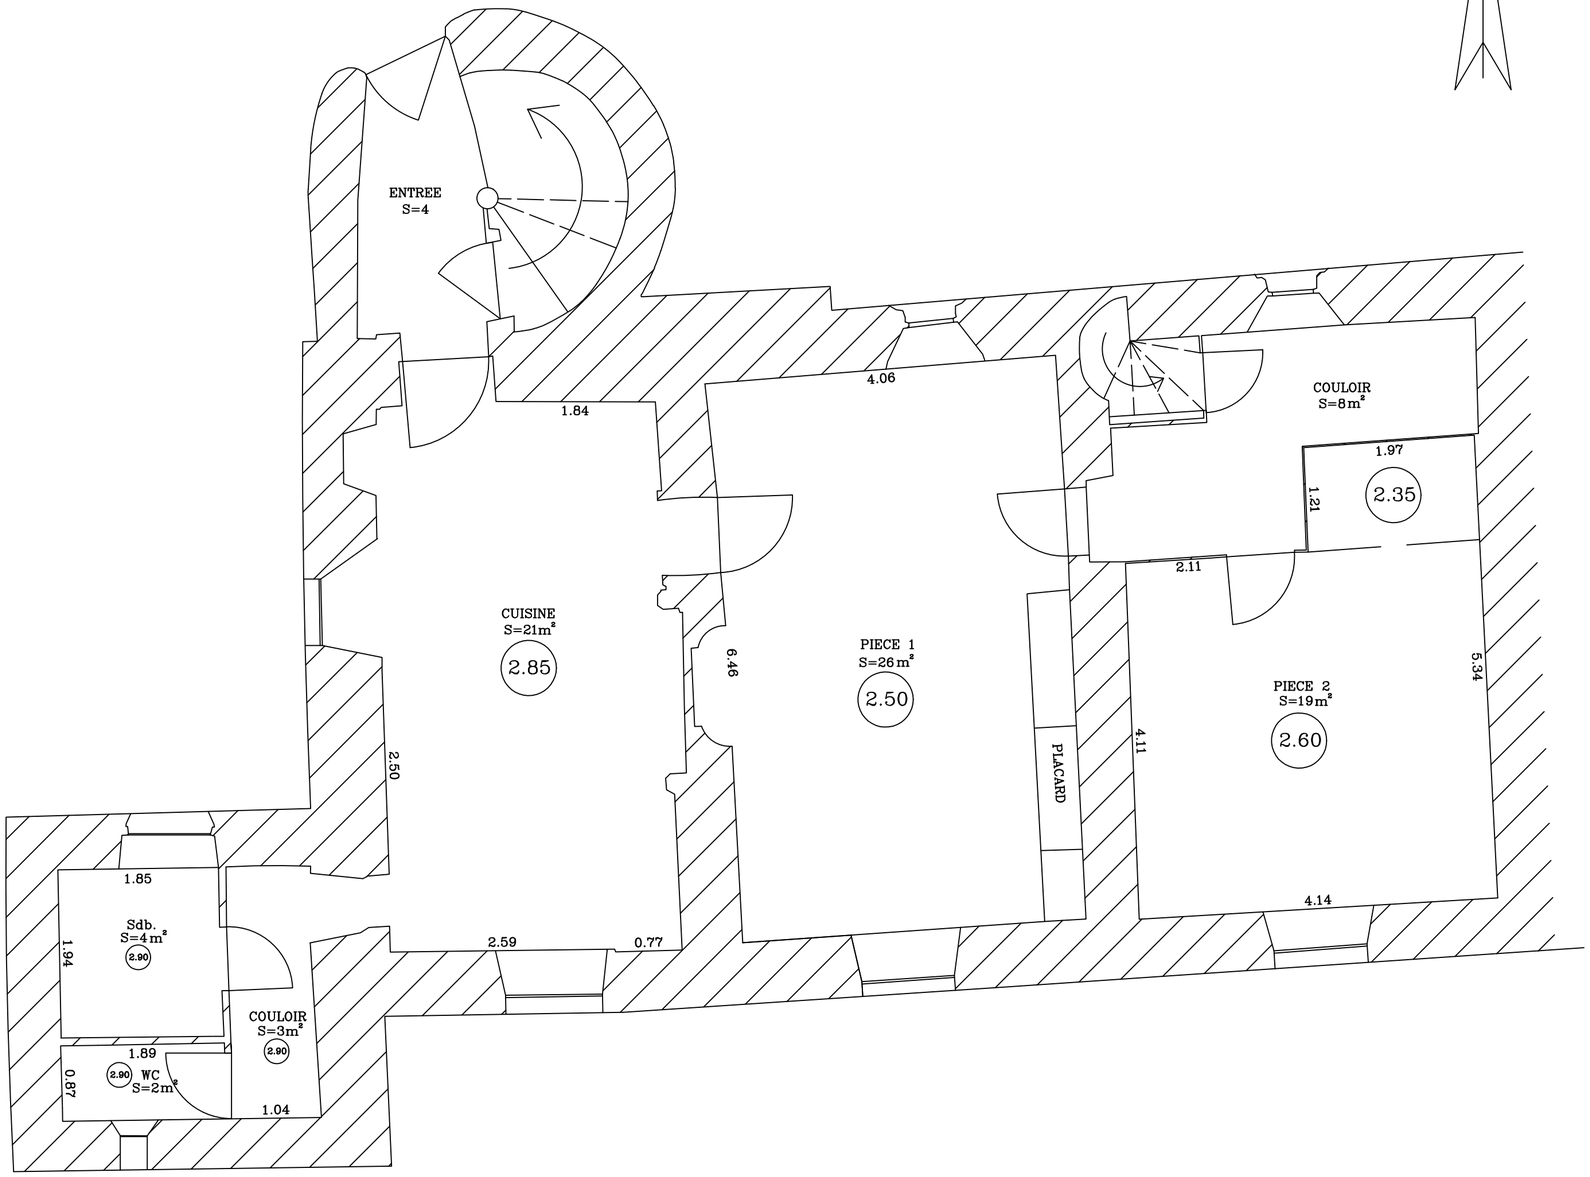

Rue de l'Église

0 2 5 10 m